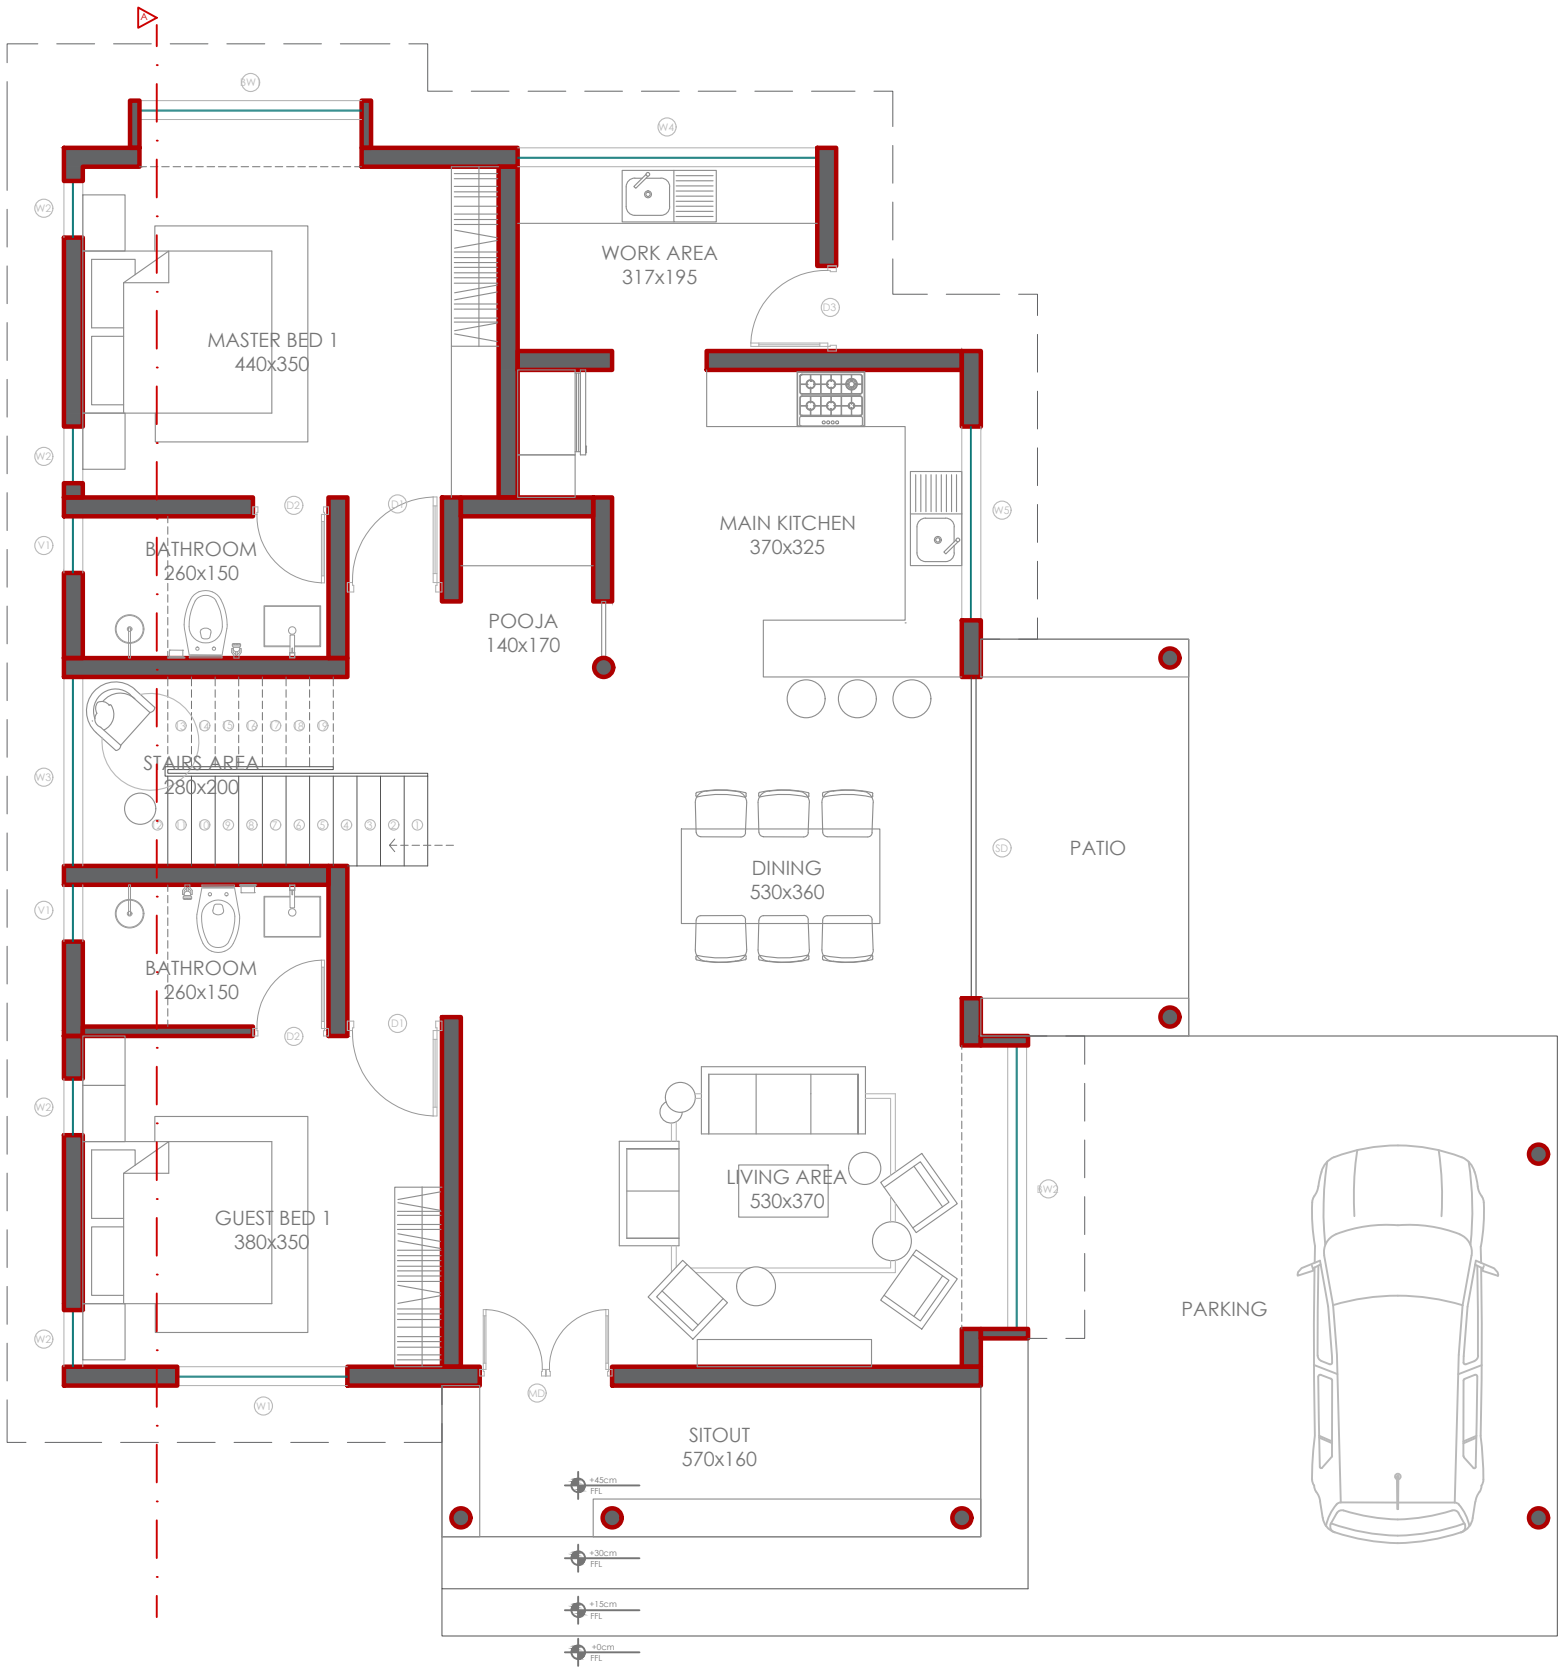


GROUND FLOOR PLAN

AREA STATEMENT (in sqft)

GROUND FLOOR	1428
FIRST FLOOR	963
TOTAL AREA	2391


DWG NO	202609/1
REVISION NO	1
DATE	15/09/2026
SCALE	1:08
DRAFTED BY	NAE
CHECKED BY	-

PROJECT NO : 202609
CLIENT : MR.JISHNU & FAMILY

GROUND FLOOR PLAN
DETAILS
sheet 1/2

NOTE.
1.This sheet is to be printed on A3 paper
2.All dimensions are in cm.
3.Contractor shall verify all dimensions on site, follow the approved drawings, and report any discrepancies or changes before execution.

NORTH

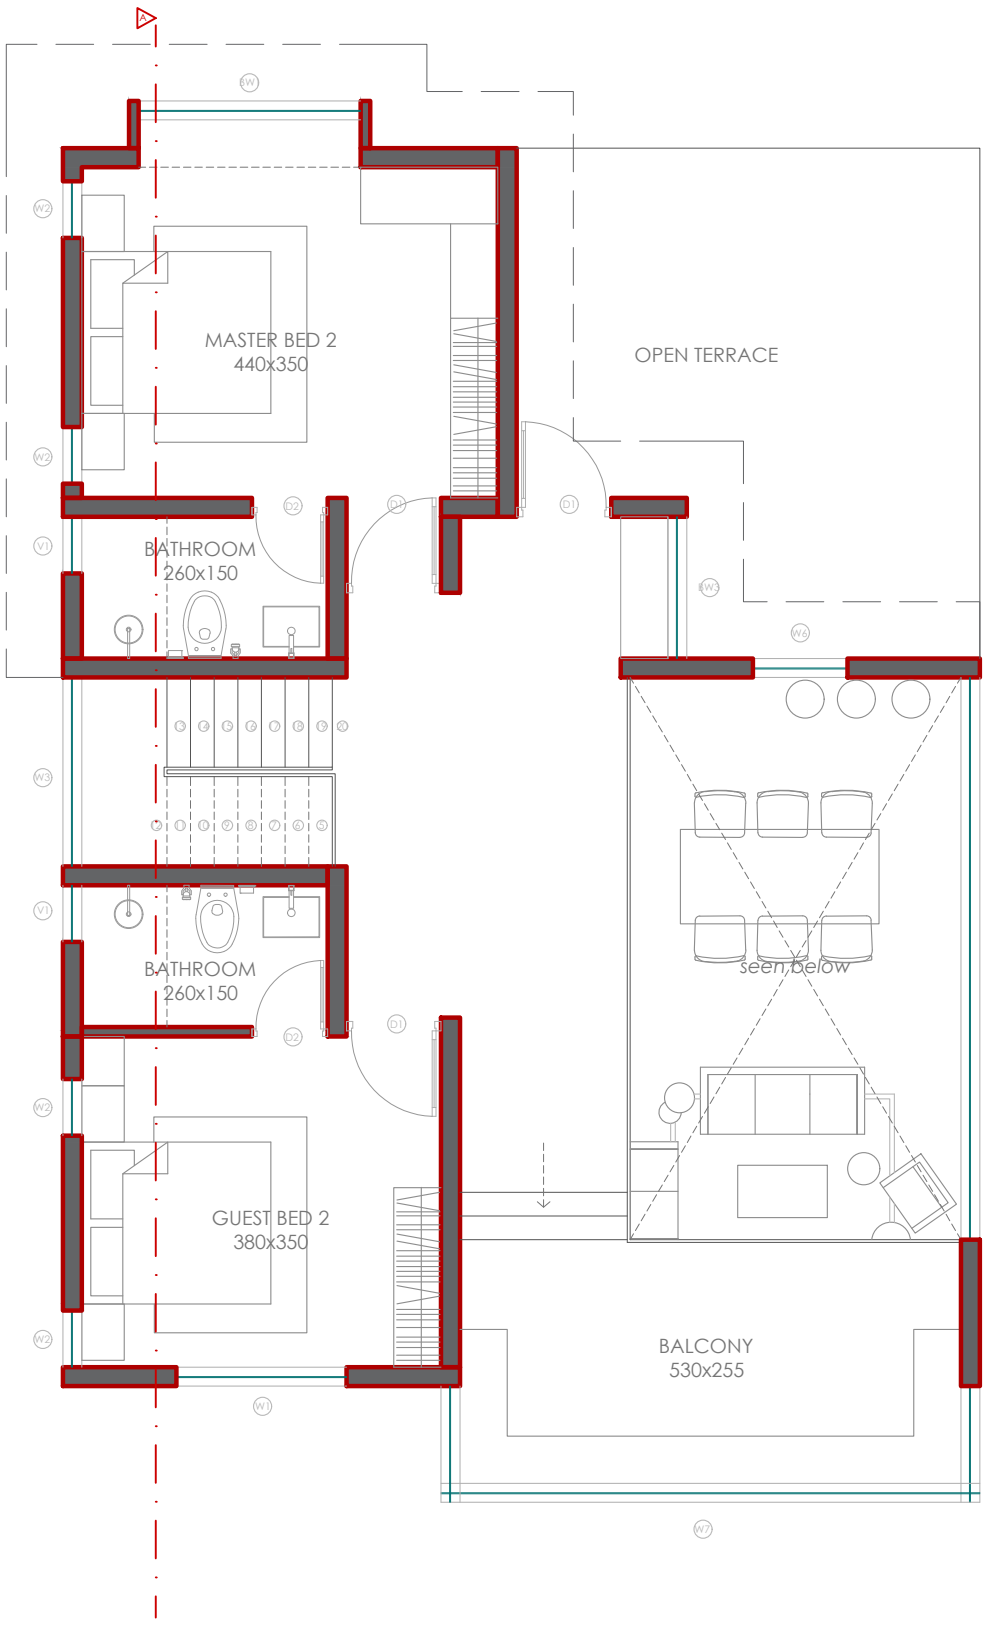

FIRST FLOOR PLAN

AREA STATEMENT (in sqft)

GROUND FLOOR	1428
FIRST FLOOR	963
TOTAL AREA	2391


DWG NO	202609/1
REVISION NO	1
DATE	15/09/2026
SCALE	1:08
DRAFTED BY	NAE
CHECKED BY	-

PROJECT NO : 202609
CLIENT : MR.JISHNU & FAMILY

FIRST FLOOR PLAN
DETAILS
sheet 2/2

NOTE.
1.This sheet is to be printed on A3 paper
2.All dimensions are in cm.
3.Contractor shall verify all dimensions on site, follow the approved drawings, and report any discrepancies or changes before execution.

NORTH

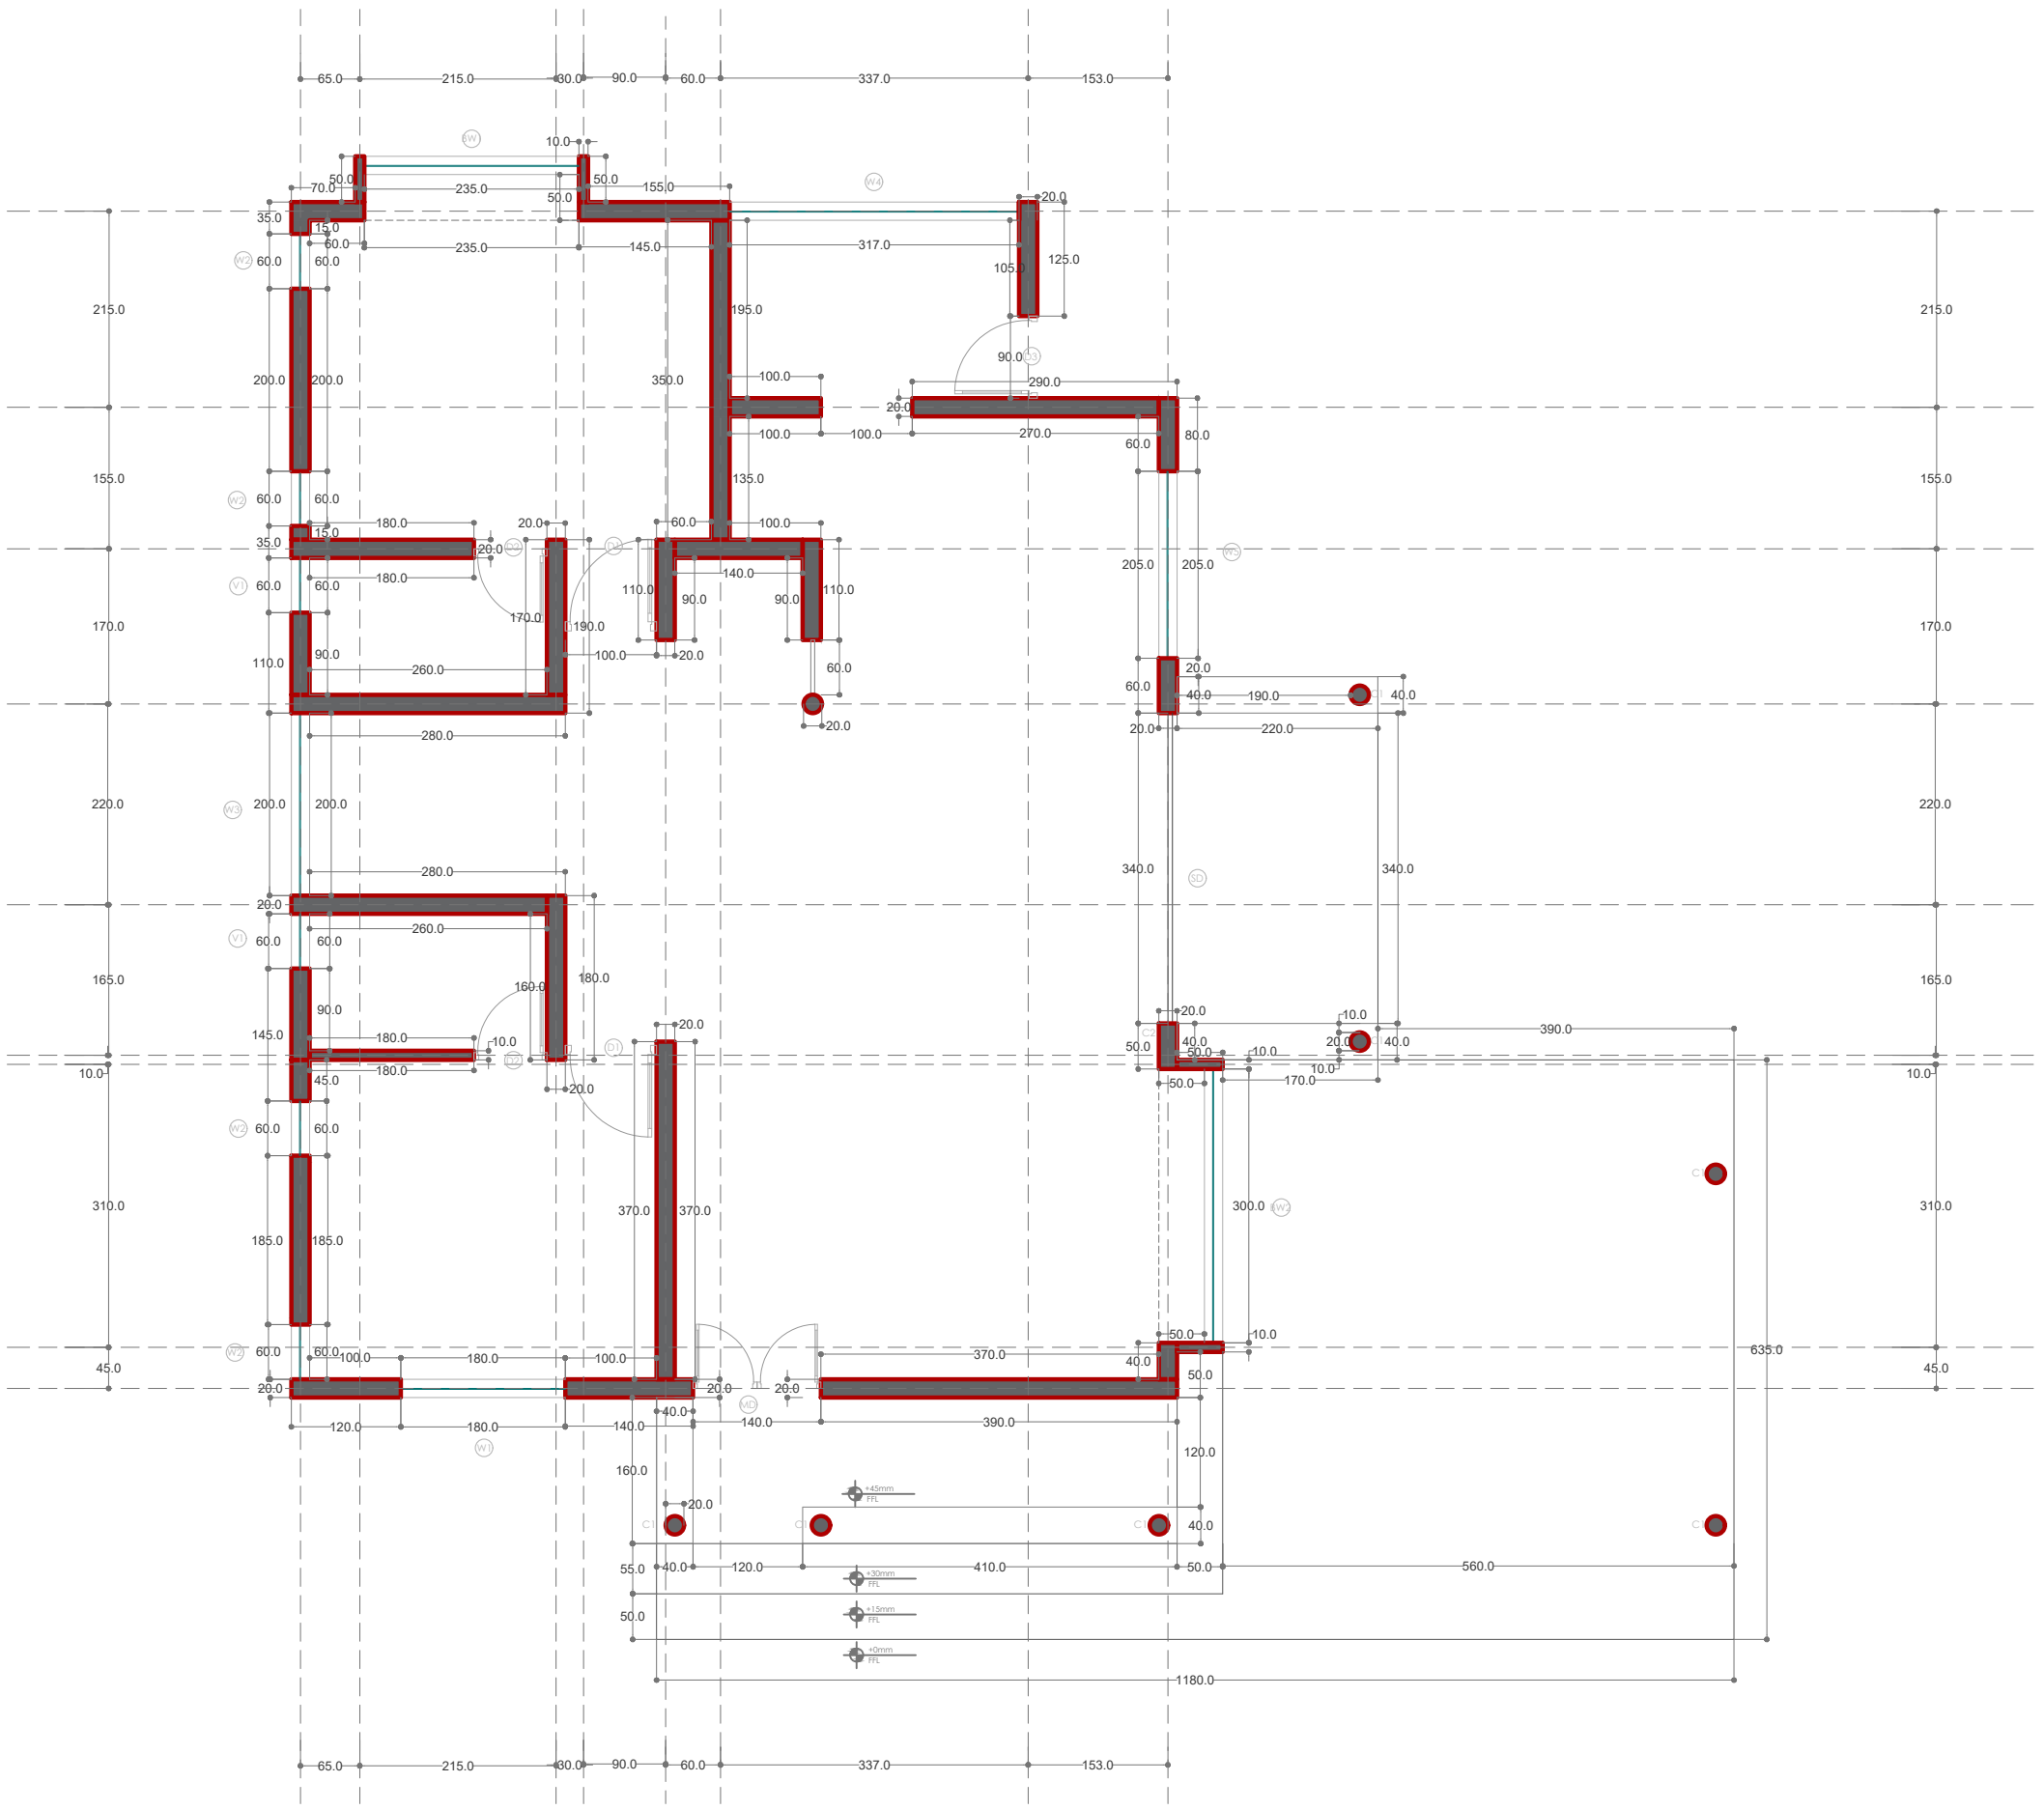

GROUND FLOOR PLAN

AREA STATEMENT (in sqft)

GROUND FLOOR	1428
FIRST FLOOR	963
TOTAL AREA	2391


DWG NO	202609/2
REVISION NO	1
DATE	15/09/2026
SCALE	1:08
DRAFTED BY	NAE
CHECKED BY	-

PROJECT NO : 202609
CLIENT : MR.JISHNU & FAMILY

MASONRY
DETAILS
sheet 1/2

NOTE.
1.This sheet is to be printed on A3 paper
2.All dimensions are in cm.
3.Contractor shall verify all dimensions on site, follow the approved drawings, and report any discrepancies or changes before execution.

NORTH

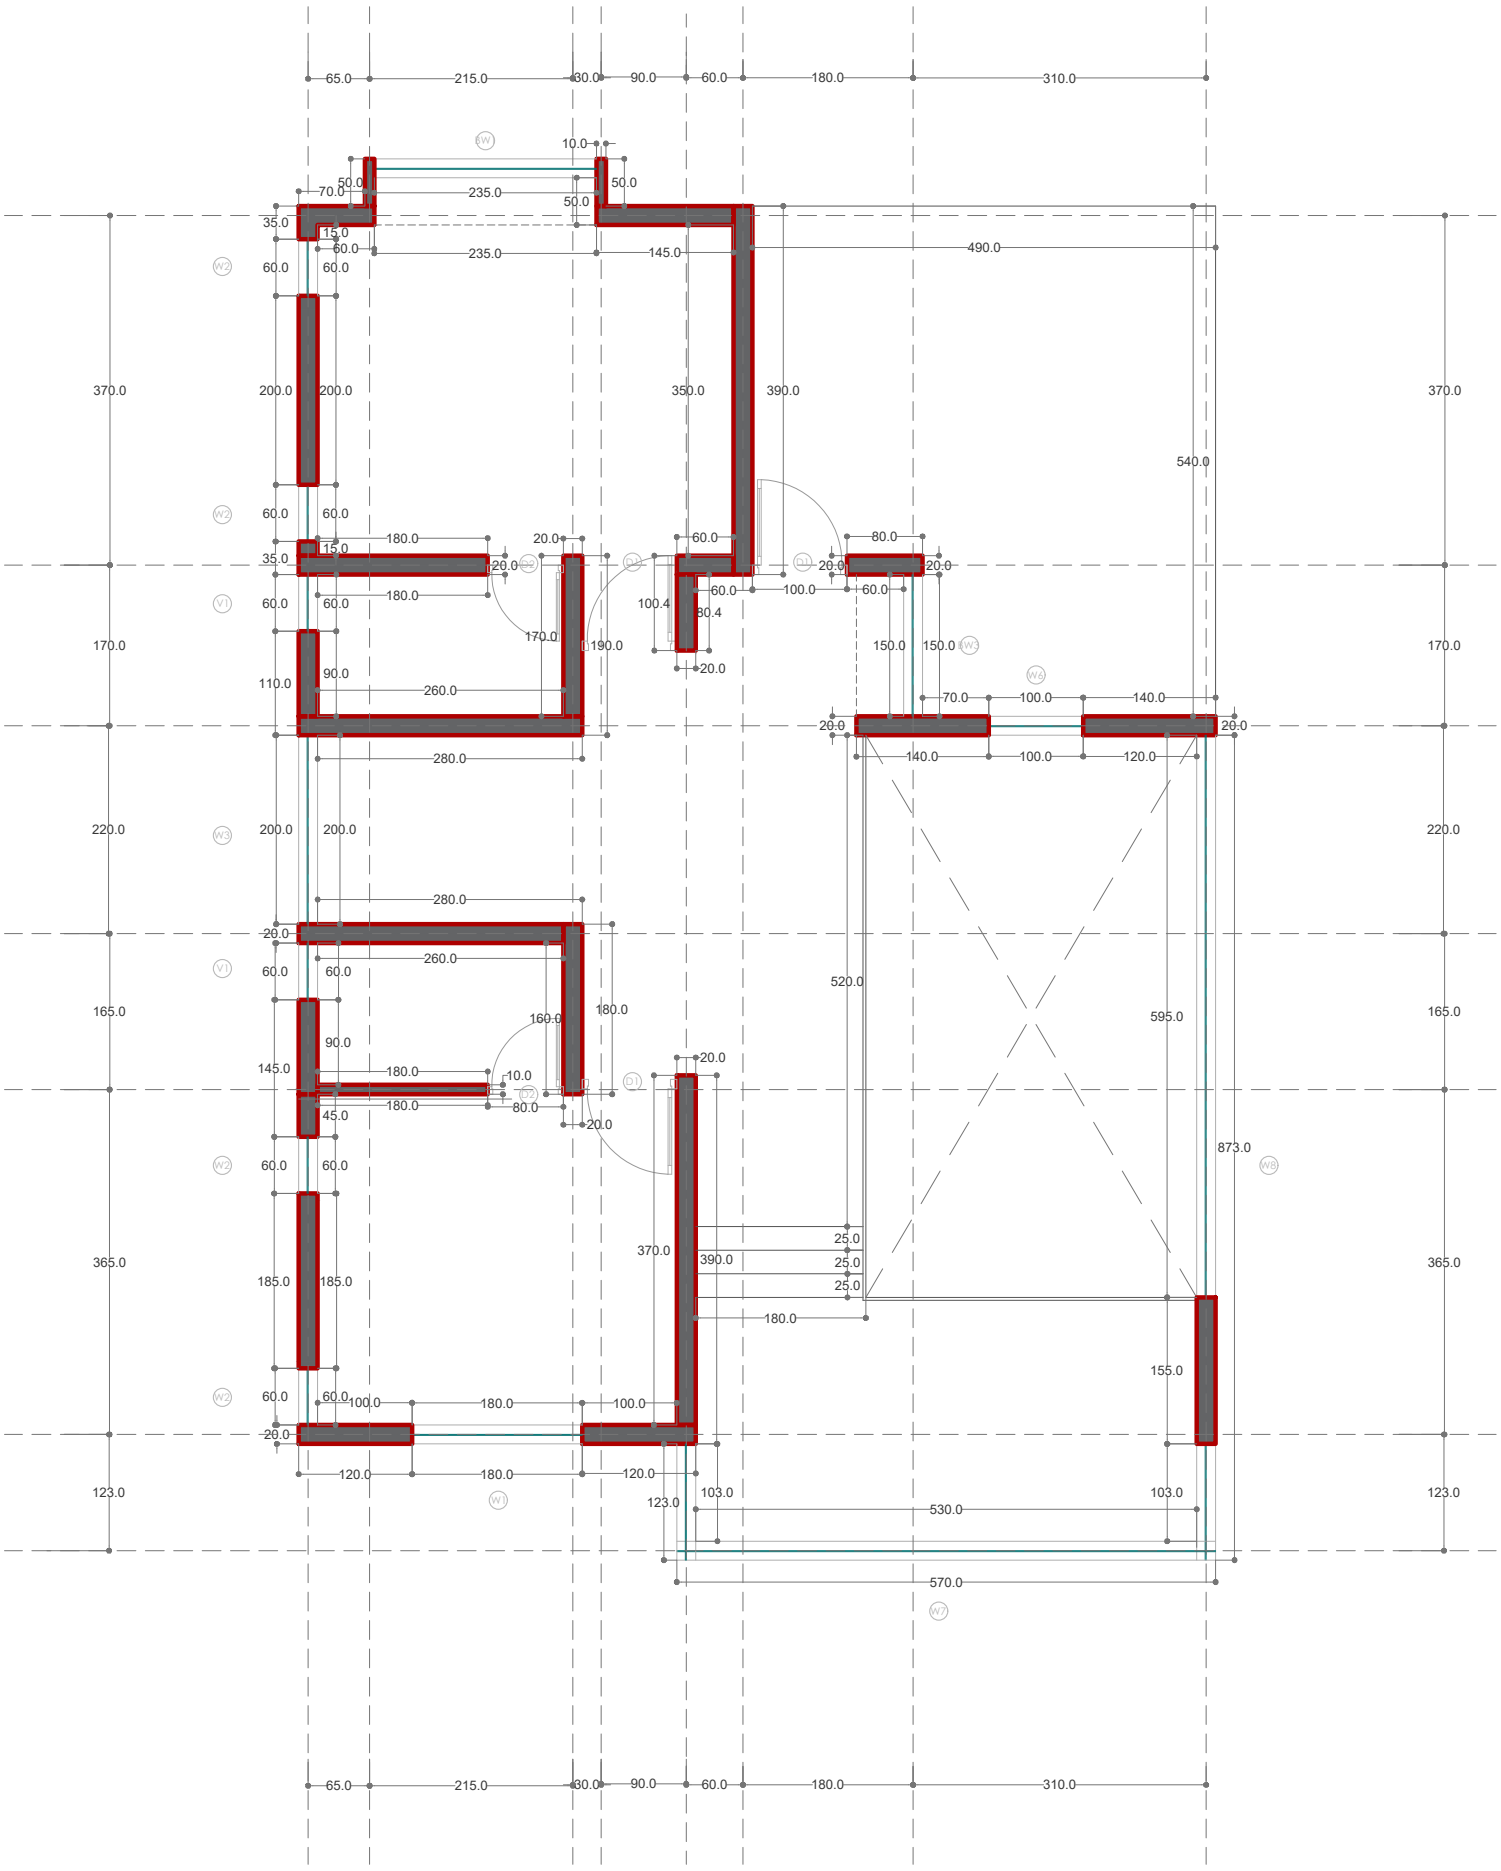

FIRST FLOOR PLAN

AREA STATEMENT (in sqft)

GROUND FLOOR	1428
FIRST FLOOR	963
TOTAL AREA	2391


DWG NO	202609/2
REVISION NO	1
DATE	15/09/2026
SCALE	1:08
DRAFTED BY	NAE
CHECKED BY	-

PROJECT NO : 202609
CLIENT : MR.JISHNU & FAMILY

MASONRY
DETAILS
sheet 2/2

NOTE.
1.This sheet is to be printed on A3 paper
2.All dimensions are in cm.
3.Contractor shall verify all dimensions on site, follow the approved drawings, and report any discrepancies or changes before execution.

NORTH

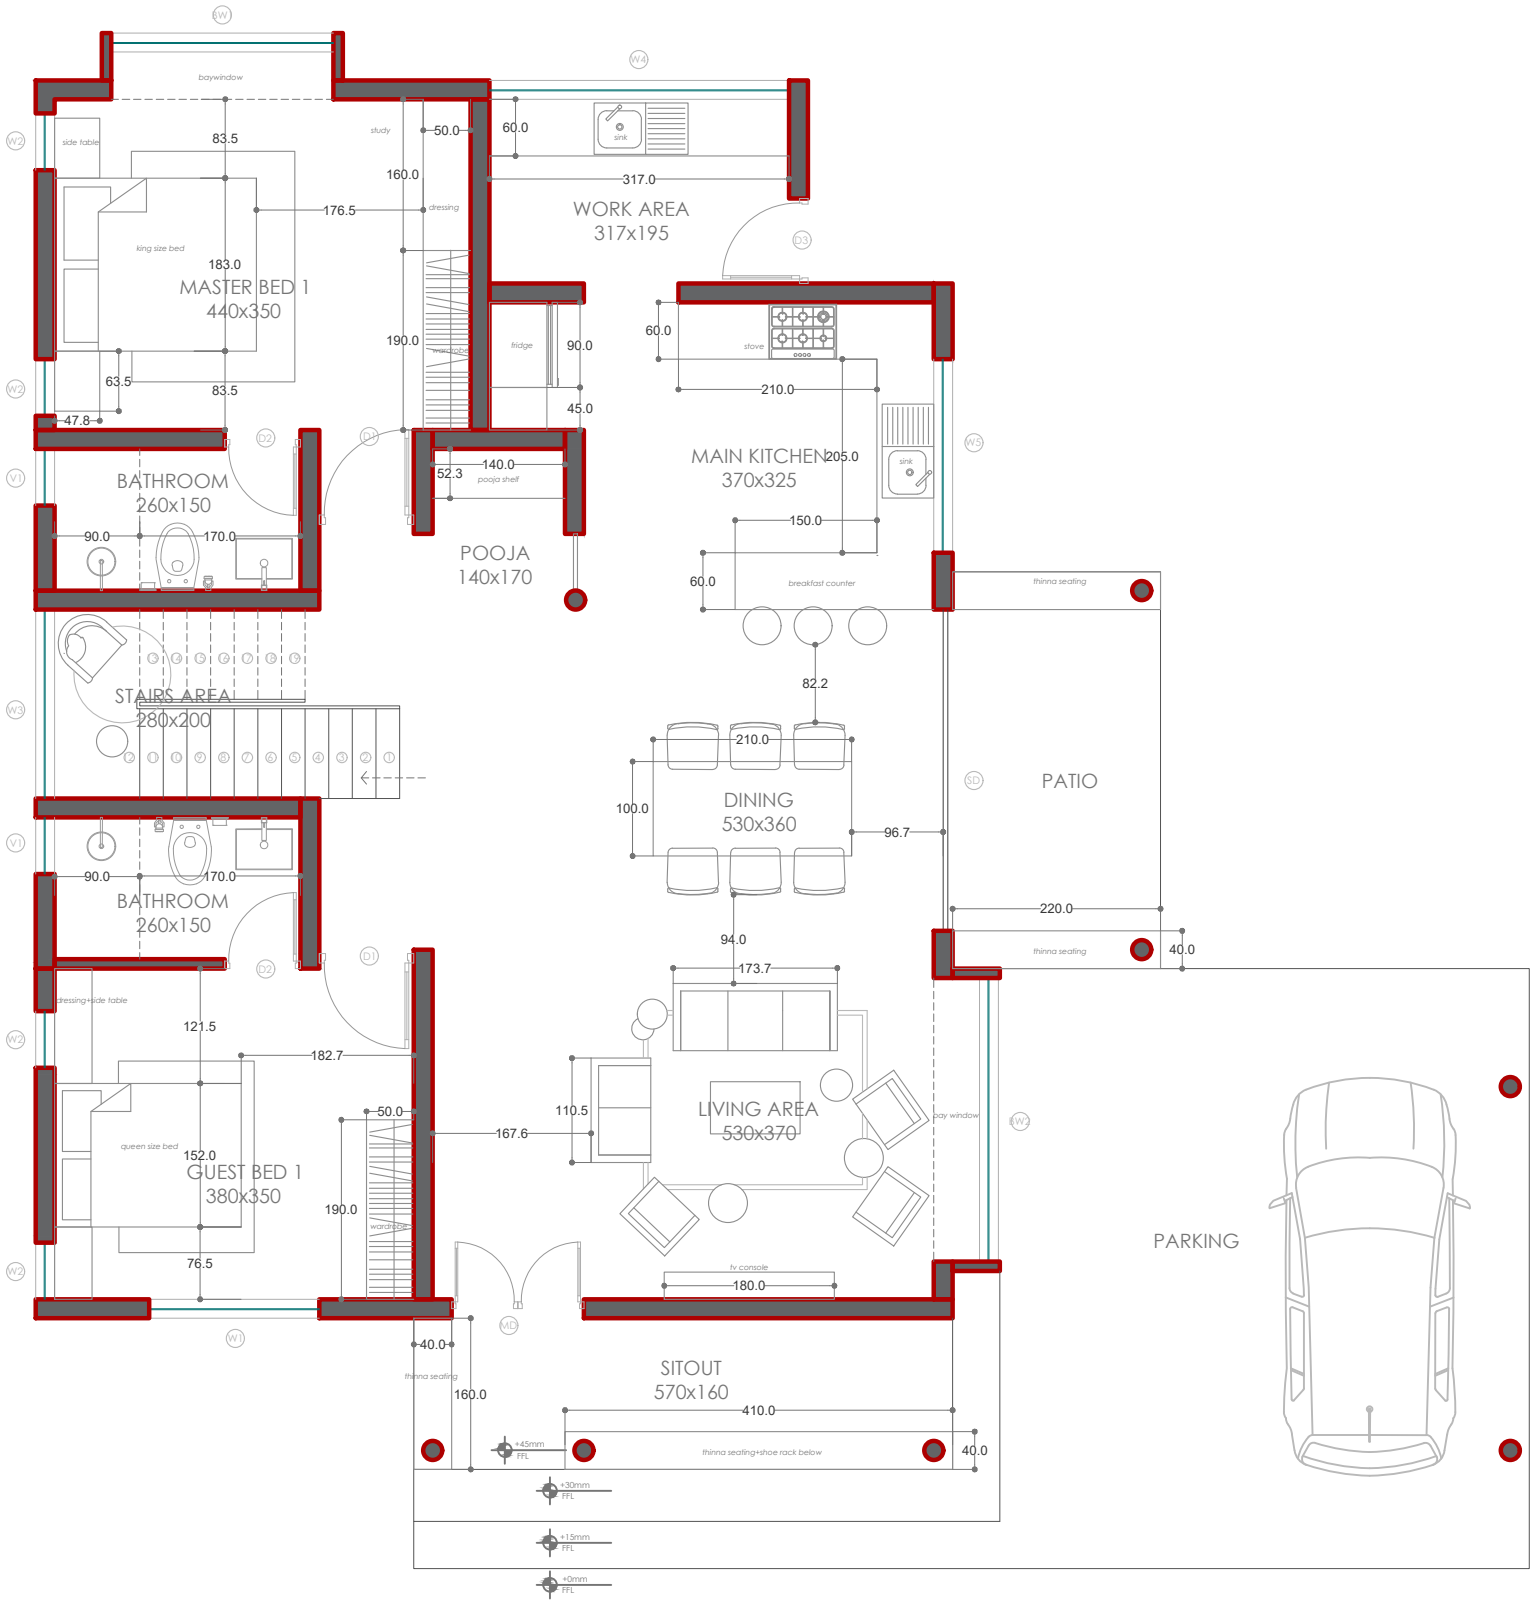

GROUND FLOOR PLAN

AREA STATEMENT (in sqft)

GROUND FLOOR	1428
FIRST FLOOR	963
TOTAL AREA	2391

DWG NO	202609/3
REVISION NO	1
DATE	15/09/2026
SCALE	1:08
DRAFTED BY	NAE
CHECKED BY	-


PROJECT NO : 202609
CLIENT : MR.JISHNU & FAMILY

FURNITURE LAYOUT

DETAILS
sheet 1/2

NOTE.
1.This sheet is to be printed on A3 paper
2.All dimensions are in cm.
3.Contractor shall verify all dimensions on site, follow the approved drawings, and report any discrepancies or changes before execution.

NORTH

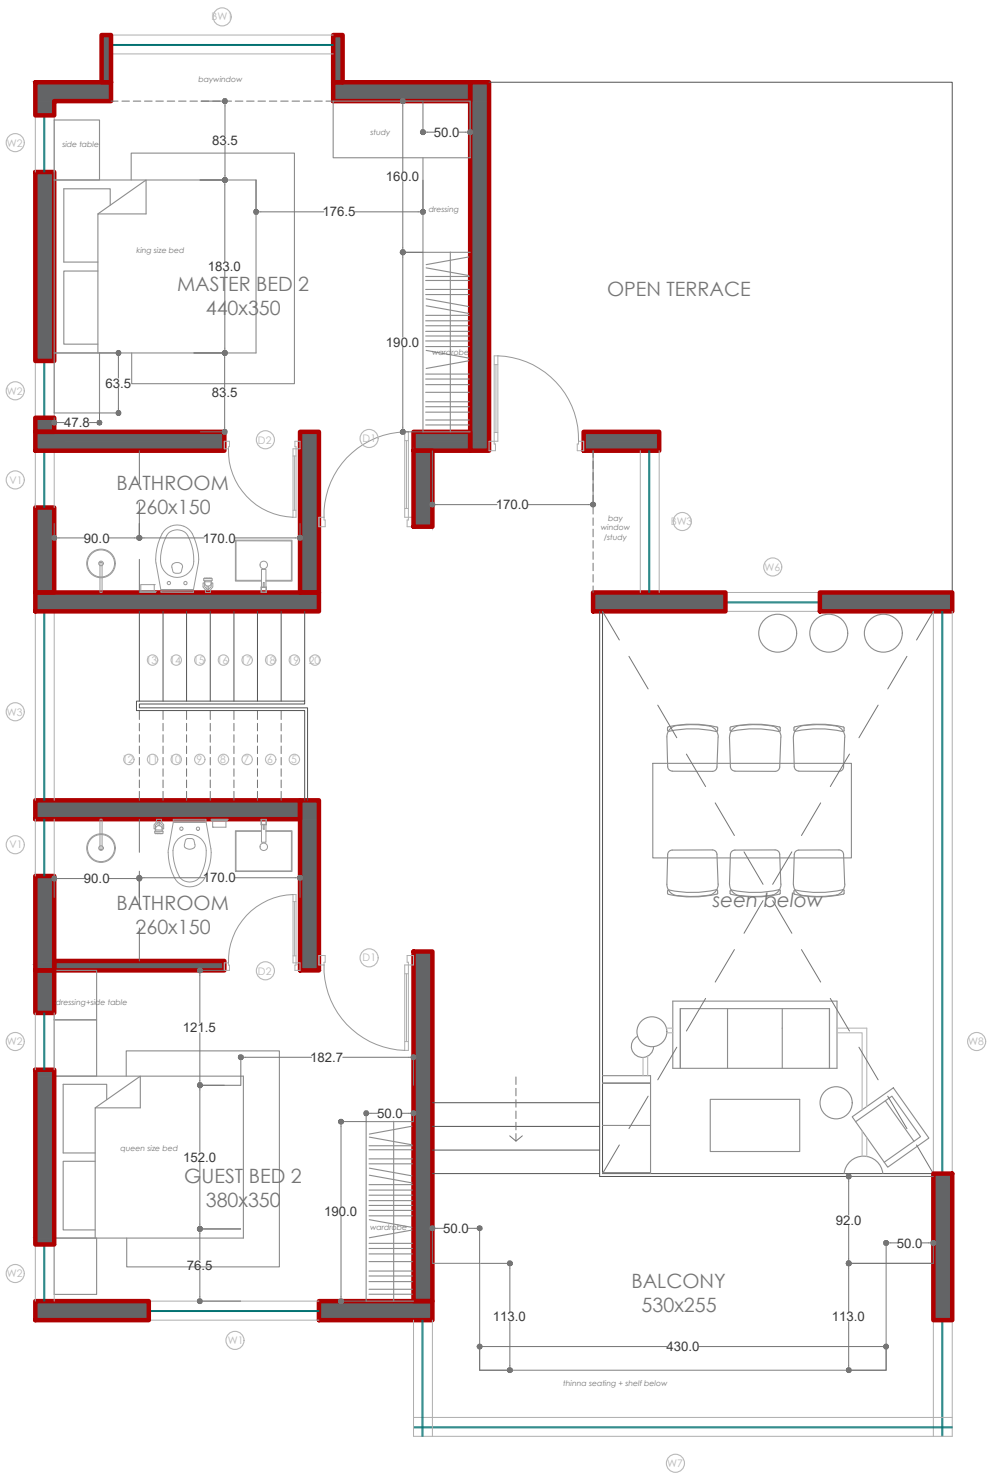

FIRST FLOOR PLAN

AREA STATEMENT (in sqft)

GROUND FLOOR	1428
FIRST FLOOR	963
TOTAL AREA	2391

DWG NO	202609/3
REVISION NO	1
DATE	15/09/2026
SCALE	1:08
DRAFTED BY	NAE
CHECKED BY	-

PROJECT NO : 202609
CLIENT : MR.JISHNU & FAMILY

FURNITURE LAYOUT

DETAILS
sheet 2/2

NOTE.
1.This sheet is to be printed on A3 paper
2.All dimensions are in cm.
3.Contractor shall verify all dimensions on site, follow the approved drawings, and report any discrepancies or changes before execution.

NORTH