


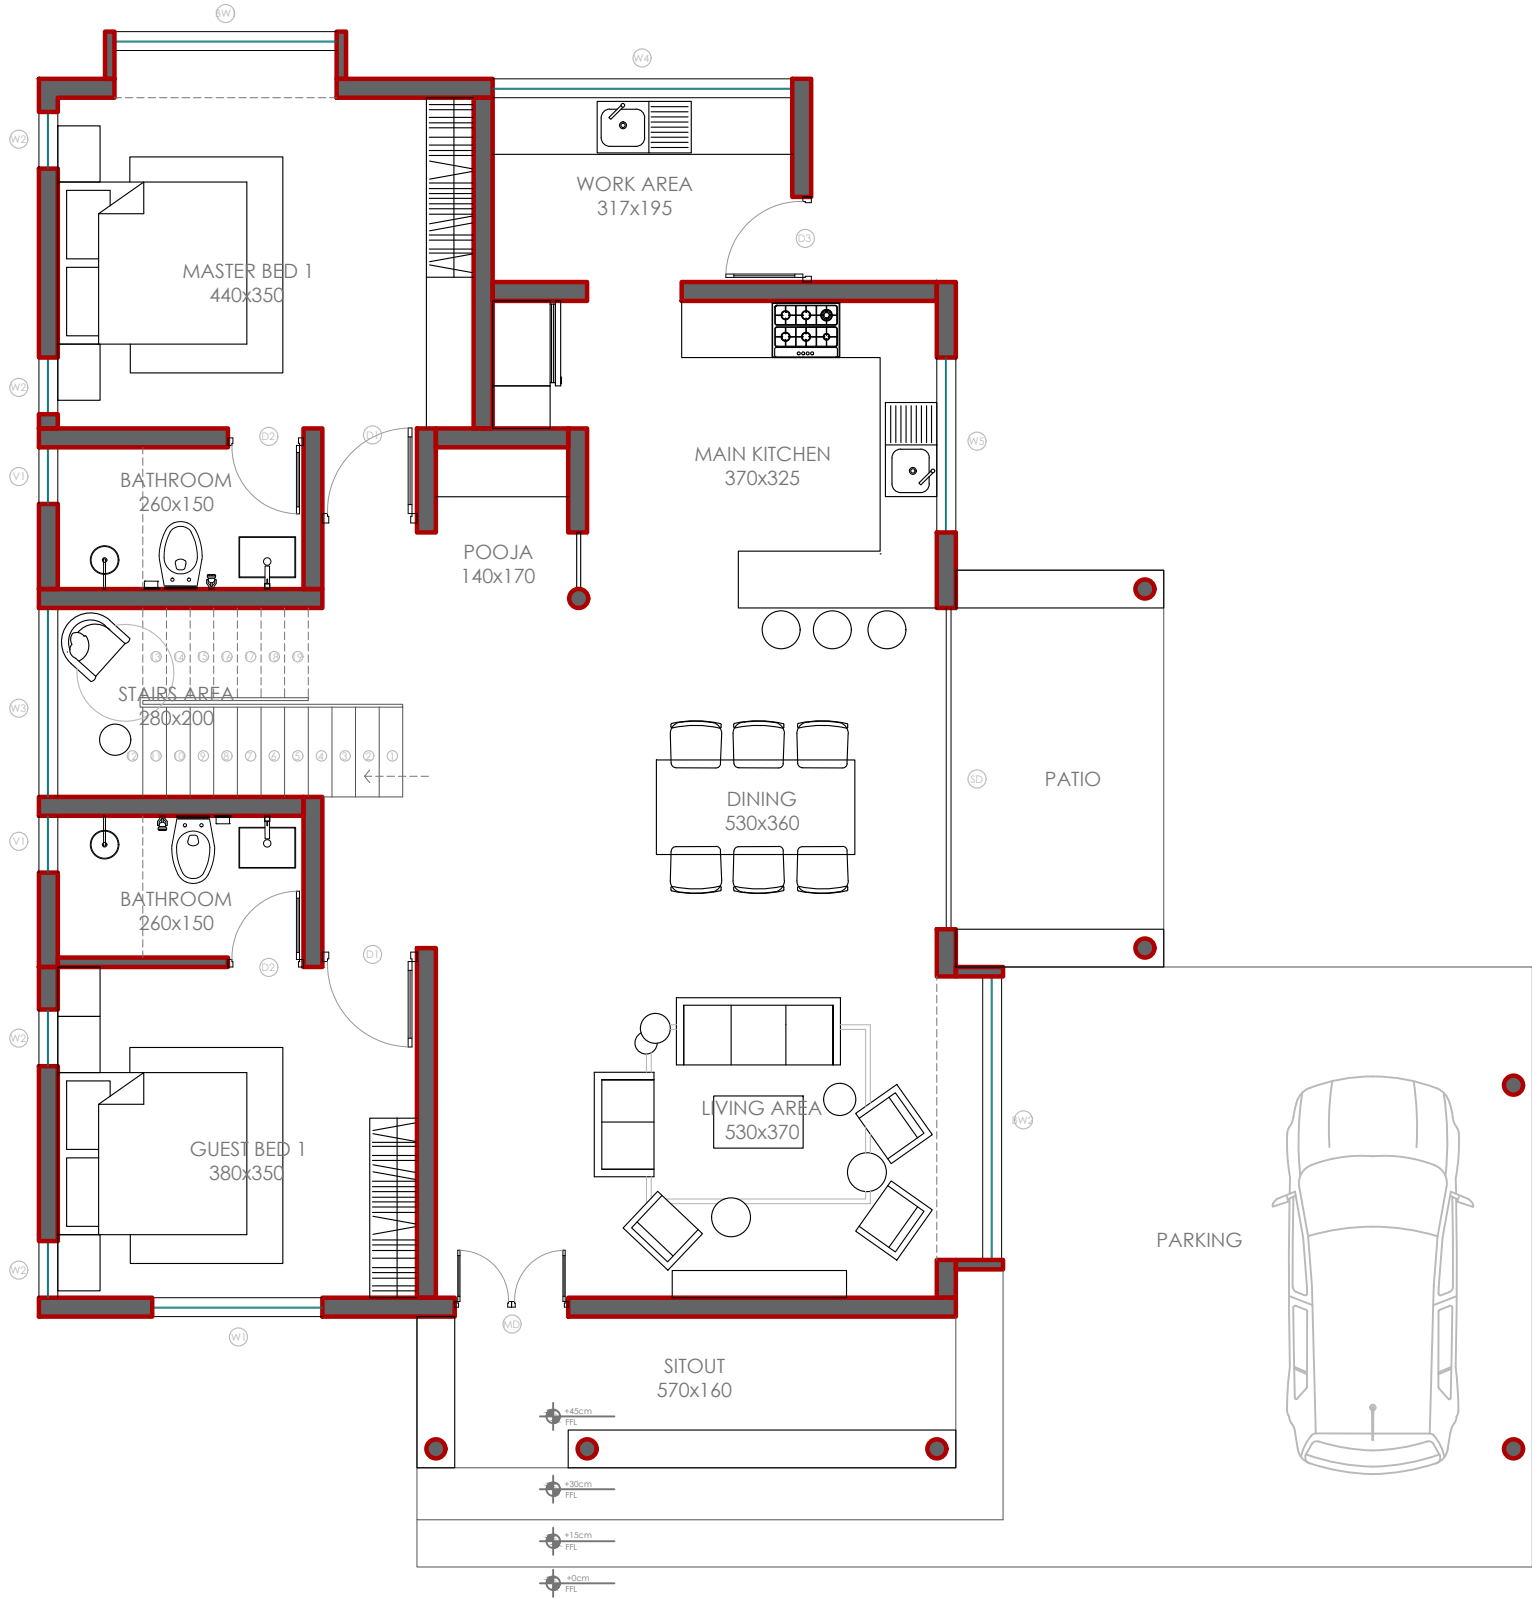

GROUND FLOOR PLAN

AREA STATEMENT (in sqft)

GROUND FLOOR	1428
FIRST FLOOR	963
TOTAL AREA	2391

DWG NO | 202609/1

REVISION NO | -

DATE | 03/09/2026

SCALE | 1:08

DRAFTED BY | NAE


CHECKED BY | -


PROJECT NO : 202609
CLIENT : MR.JISHNU & FAMILY

GROUND FLOOR PLAN

DETAILS
sheet 1/2

NOTE.
1.This sheet is to be printed on A3 paper
2.All dimensions are in cm.
3.Contractor shall verify all dimensions on site, follow the approved drawings, and report any discrepancies or changes before execution.

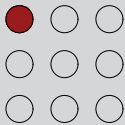

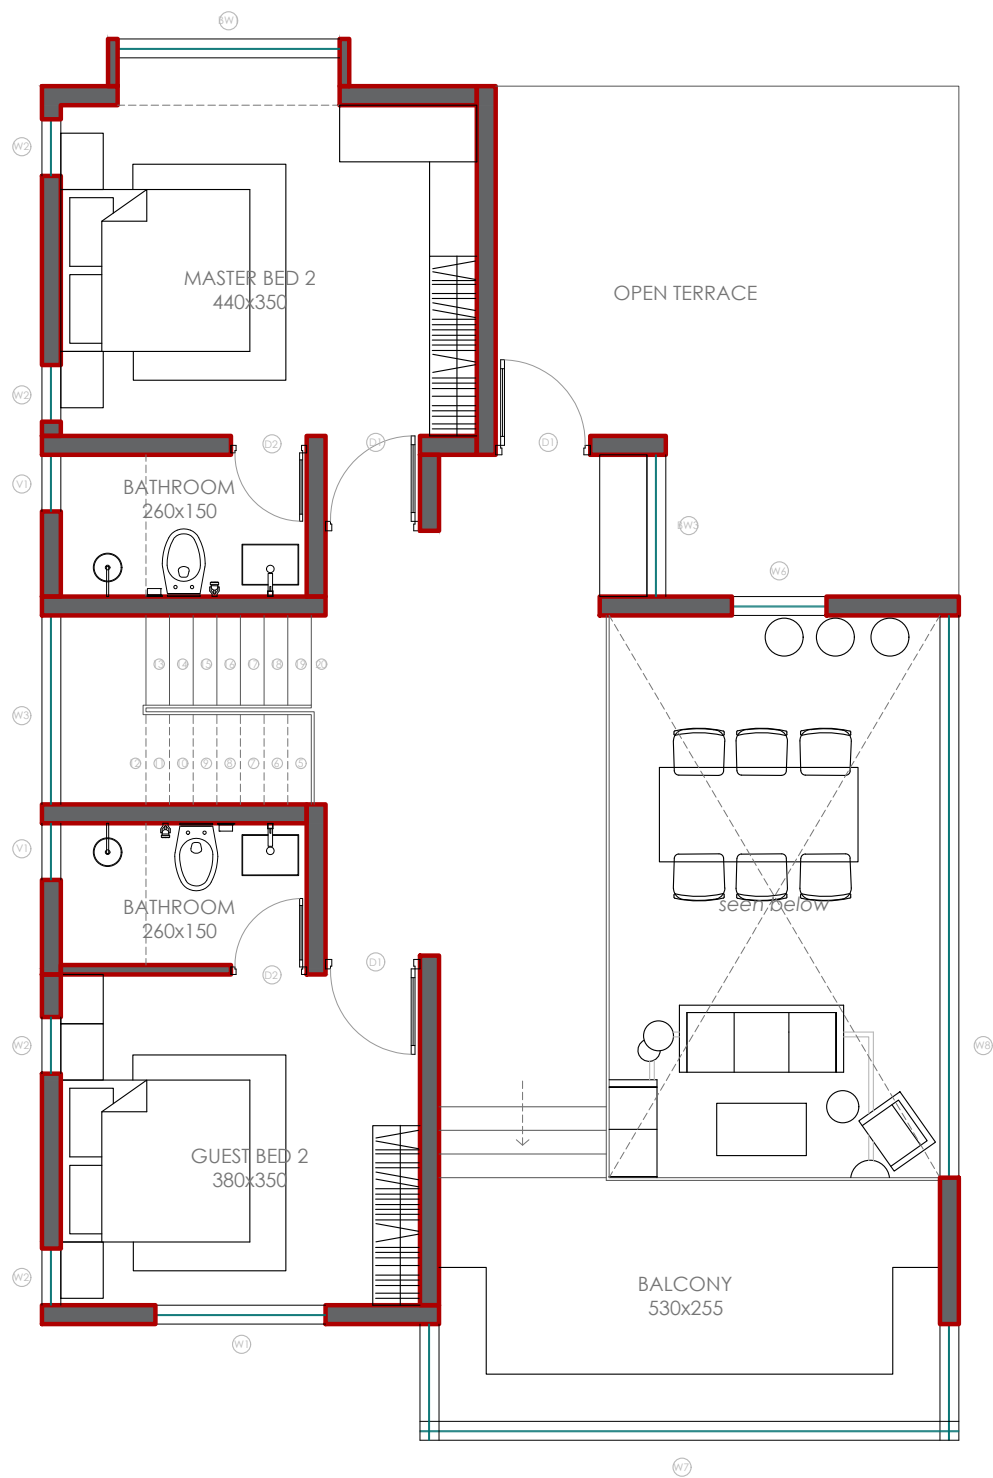

FIRST FLOOR PLAN

AREA STATEMENT (in sqft)


GROUND FLOOR	1428
FIRST FLOOR	963
TOTAL AREA	2391

DWG NO	202609/1
REVISION NO	-
DATE	03/09/2026
SCALE	1:08
DRAFTED BY	NAE
CHECKED BY	-

PROJECT NO : 202609
CLIENT : MR.JISHNU & FAMILY

FIRST FLOOR PLAN
DETAILS
sheet 2/2

NOTE.
1.This sheet is to be printed on A3 paper
2.All dimensions are in cm.
3.Contractor shall verify all dimensions on site, follow the approved drawings, and report any discrepancies or changes before execution.

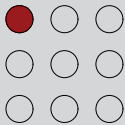

GROUND FLOOR PLAN

AREA STATEMENT (in sqft)


GROUND FLOOR	1428
FIRST FLOOR	963
TOTAL AREA	2391


DWG NO	202609/2
REVISION NO	-
DATE	03/09/2026
SCALE	1:08
DRAFTED BY	NAE
CHECKED BY	-

PROJECT NO : 202609
CLIENT : MR.JISHNU & FAMILY

MASONRY
DETAILS
sheet 1/2

NOTE.
1.This sheet is to be printed on A3 paper
2.All dimensions are in cm.
3.Contractor shall verify all dimensions on site, follow the approved drawings, and report any discrepancies or changes before execution.

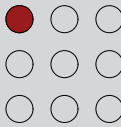

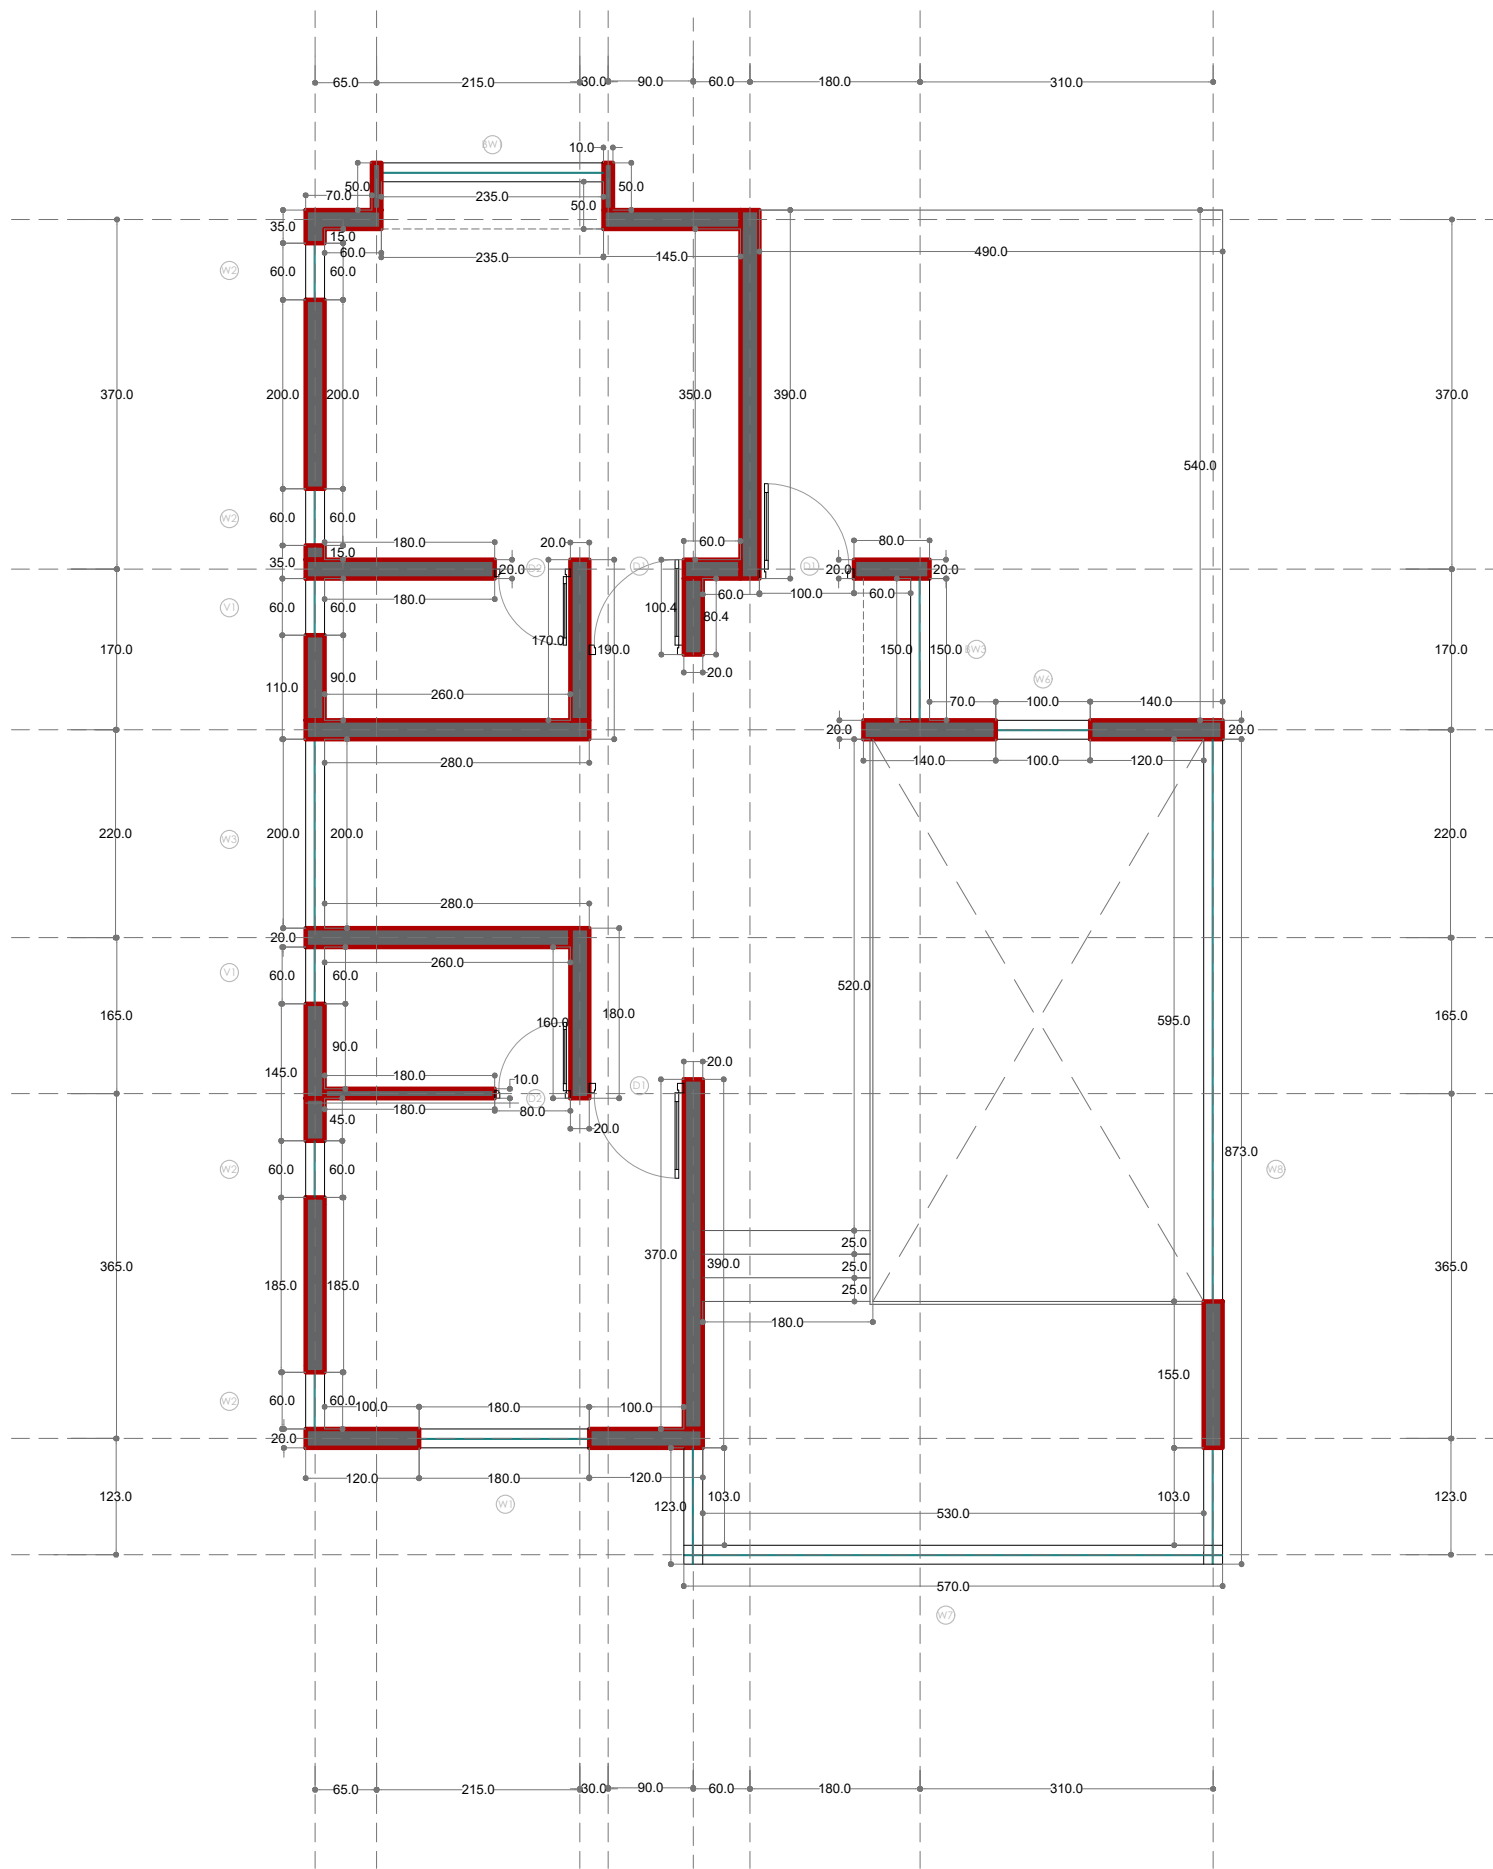

FIRST FLOOR PLAN

AREA STATEMENT (in sqft)


GROUND FLOOR	1428
FIRST FLOOR	963
TOTAL AREA	2391


DWG NO	202609/2
REVISION NO	-
DATE	03/09/2026
SCALE	1:08
DRAFTED BY	NAE
CHECKED BY	-

PROJECT NO : 202609
CLIENT : MR.JISHNU & FAMILY

MASONRY
DETAILS
sheet 2/2

NOTE.
1.This sheet is to be printed on A3 paper
2.All dimensions are in cm.
3.Contractor shall verify all dimensions on site, follow the approved drawings, and report any discrepancies or changes before execution.

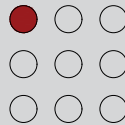

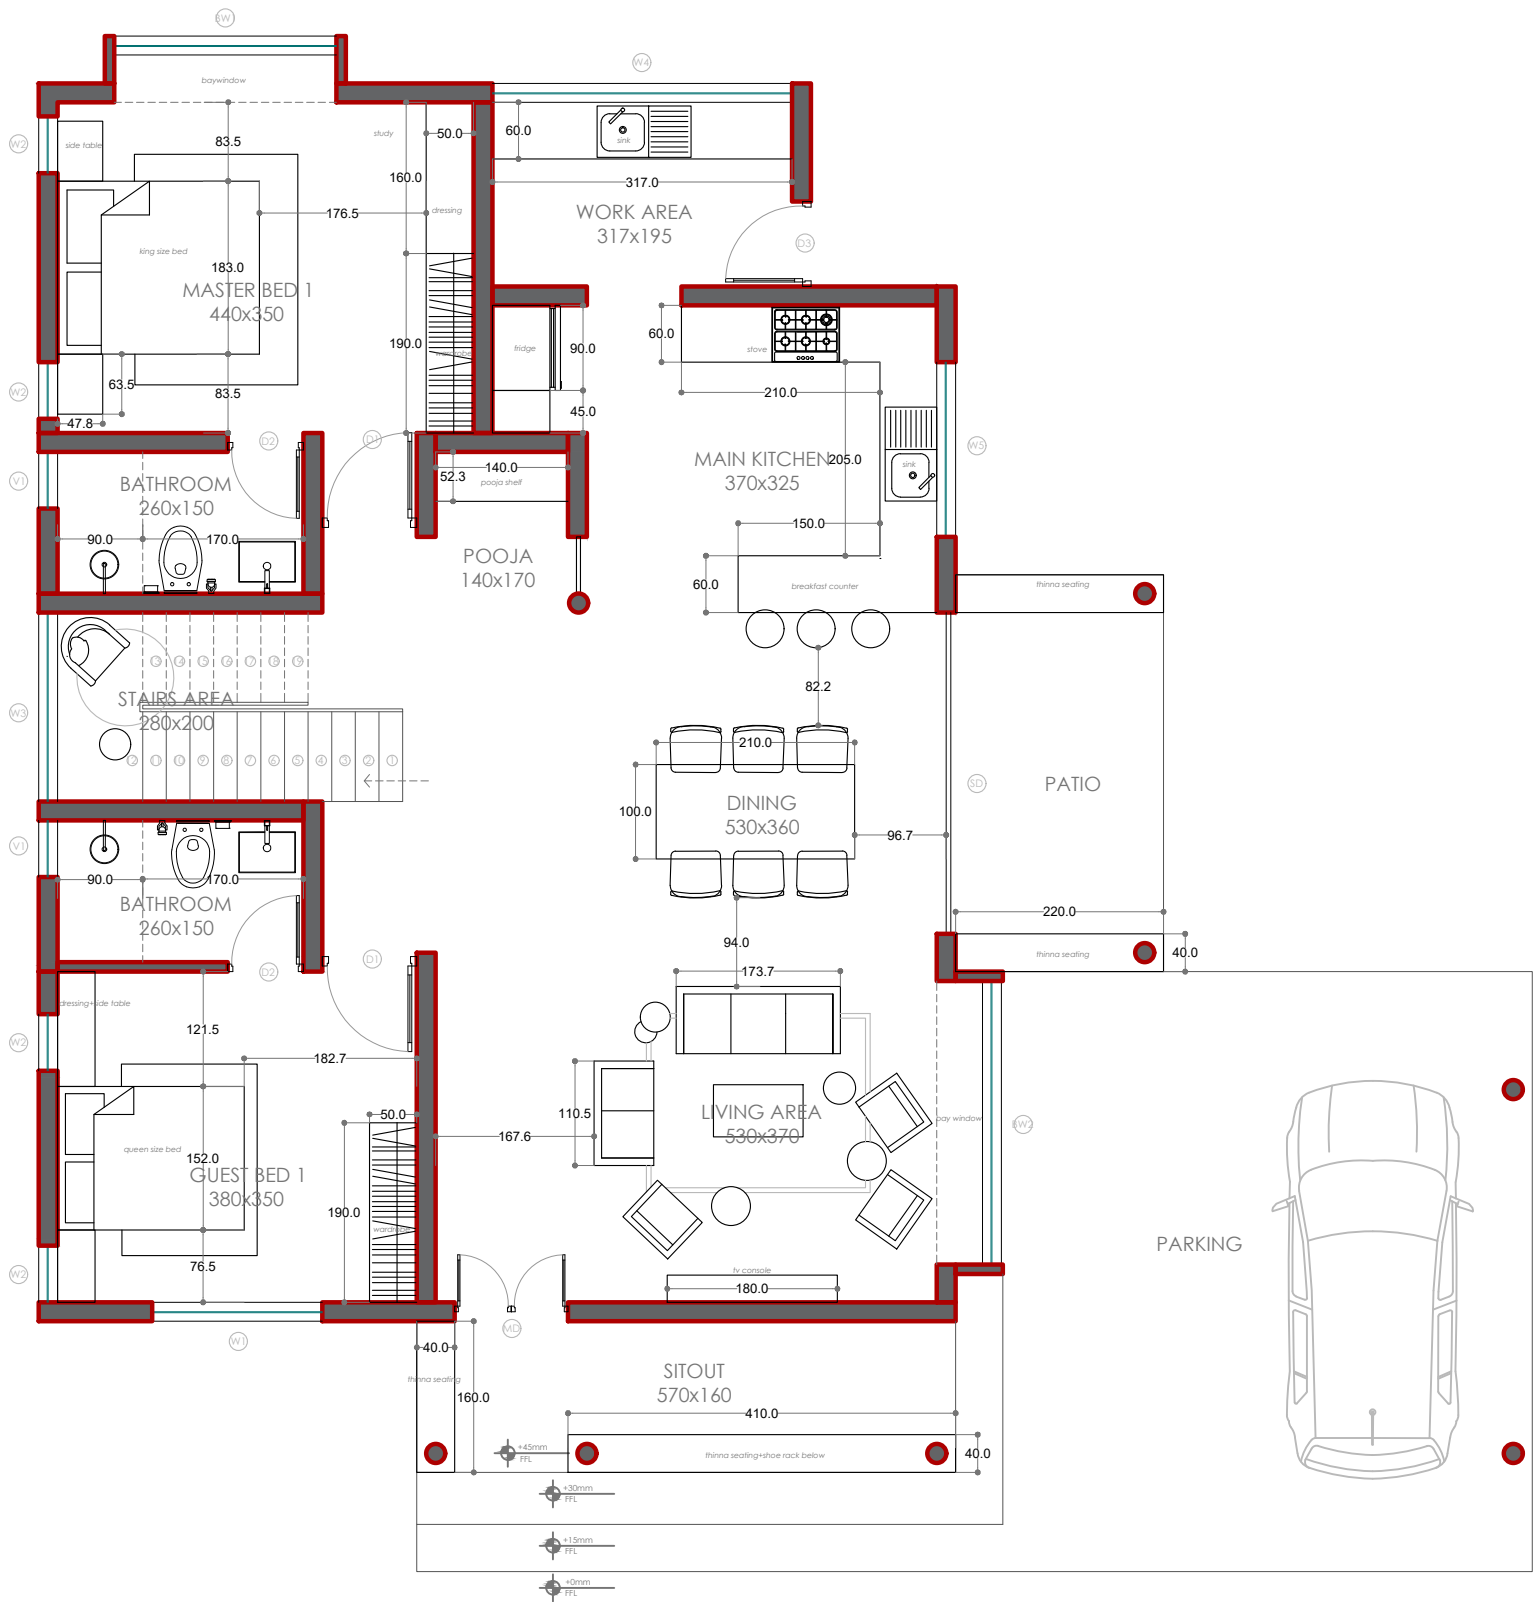

GROUND FLOOR PLAN

AREA STATEMENT (in sqft)

GROUND FLOOR	1428
FIRST FLOOR	963
TOTAL AREA	2391

DWG NO | 202609/3

REVISION NO | -

DATE | 03/09/2026

SCALE | 1:08

DRAFTED BY | NAE


CHECKED BY | -


PROJECT NO : 202609
CLIENT : MR.JISHNU & FAMILY

FURNITURE LAYOUT

DETAILS
sheet 1/2

NOTE.
1.This sheet is to be printed on A3 paper
2.All dimensions are in cm.
3.Contractor shall verify all dimensions on site, follow the approved drawings, and report any discrepancies or changes before execution.

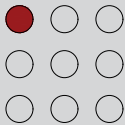

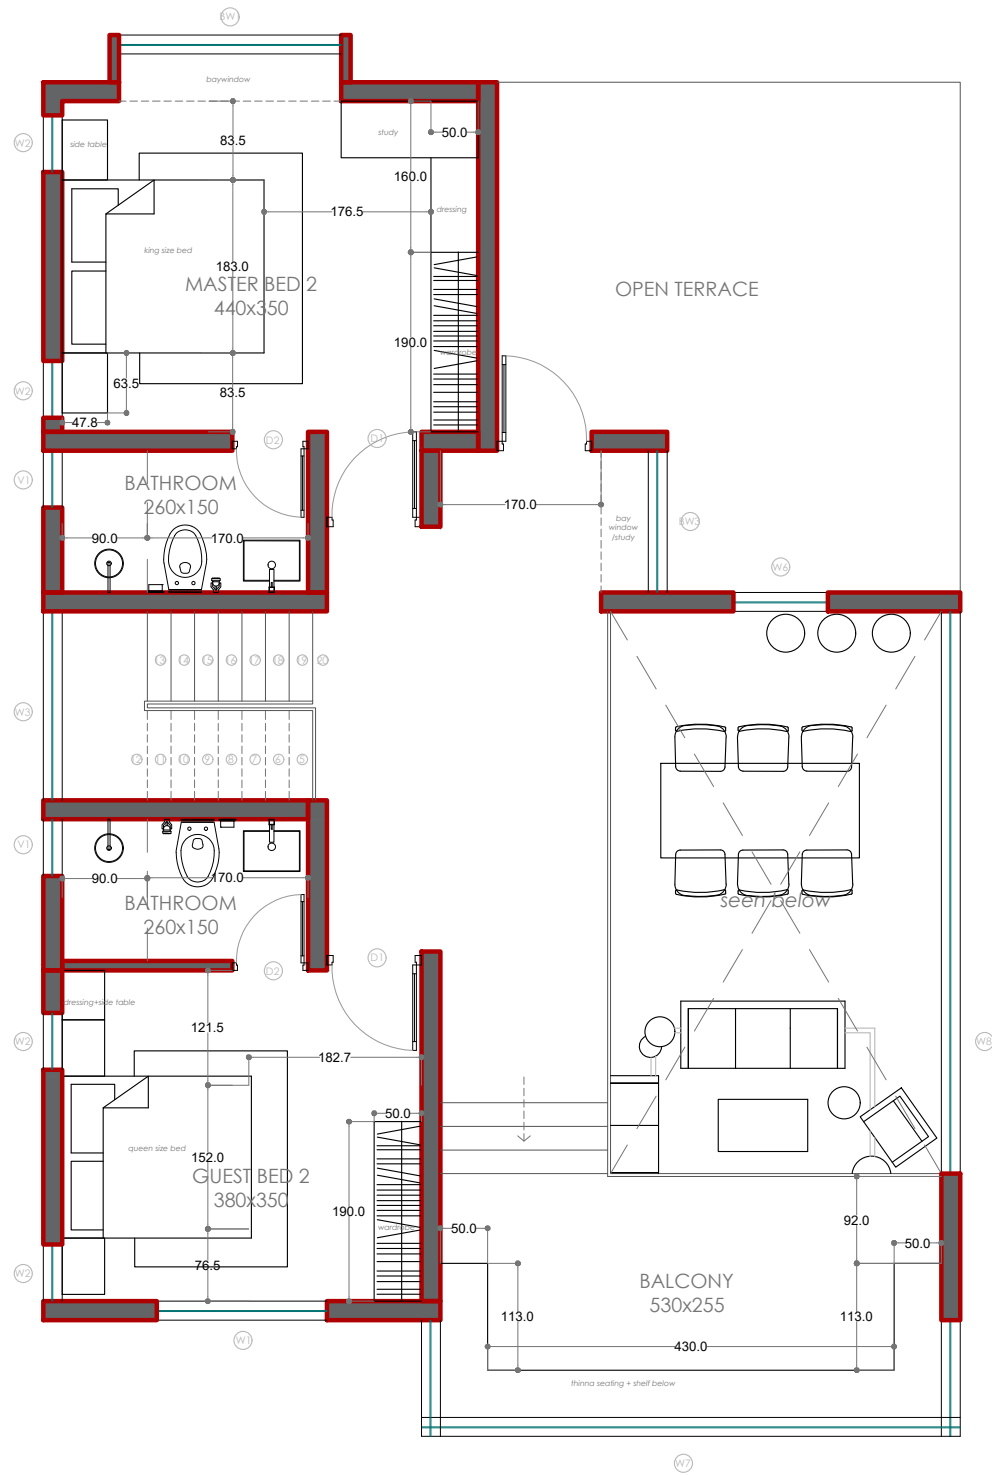

FIRST FLOOR PLAN

AREA STATEMENT (in sqft)


GROUND FLOOR	1428
FIRST FLOOR	963
TOTAL AREA	2391

DWG NO	202609/3
REVISION NO	-
DATE	03/09/2026
SCALE	1:08
DRAFTED BY	NAE
CHECKED BY	-

PROJECT NO : 202609
CLIENT : MR.JISHNU & FAMILY

FURNITURE LAYOUT
DETAILS
sheet 2/2

NOTE.
1.This sheet is to be printed on A3 paper
2.All dimensions are in cm.
3.Contractor shall verify all dimensions on site, follow the approved drawings, and report any discrepancies or changes before execution.

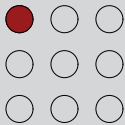

SCHEDULE OF OPENINGS

NOTE: ALL DIMENSIONS ARE IN CENTIMETRES.

NAME	DESCRIPTION	WIDTH	SILL HEIGHT	LINTEL HEIGHT	QTY
MD	MAIN DOOR WITH WINDOWS	120	0	260	1
D1	DOOR 1	100	0	260	5
D2	DOOR 2	80	0	220	4
D3	DOOR 3	90	0	220	1
SD	SLIDING DOOR	340	0	220	1
W1	WINDOW 1	180	50	220	2
W2	WINDOW 2	60	50	220	8
W3	WINDOW 3 JAALI	200	0	610	1
W4	WINDOW 4	213	80	220	1
W5	WINDOW 5	185	80	220	1
W6	WINDOW 6	100	50	220	1
V1	VENTILATOR	60	140	220	1
BW1	BAY WINDOW 1	235	50	220	2
BW2	BAY WINDOW 2	300	50	220	1
BW3	BAY WINDOW 3	150	50	220	1